


SCHEDULE OF BEAMS AT 1ST FLOOR LEVEL :- BEAM BB3,4,5,14,1

SCHEDULE OF SLABS AT 1ST FLOOR LEVEL

SLAB MARKED	THICK.	TYPE	REINFORCEMENT
			SHORT BAR
S2	175	TWO WAY	T10@100C/C (ALT. BENT UP)
S3	125	TWO WAY	T8@150C/C (ALT. BENT UP)
S4	125	ONE WAY	T8@100C/C (ALT. BENT UP)
S5	115	ONE WAY	T8@150C/C (ALT. BENT UP)
S6	115	ONE WAY	T8@150C/C (ALL STRAIGHT)
S7	175	TWO WAY	T10@150C/C (ALT. BENT UP)
ST	225	ONE WAY	T12@100C/C (MAIN)

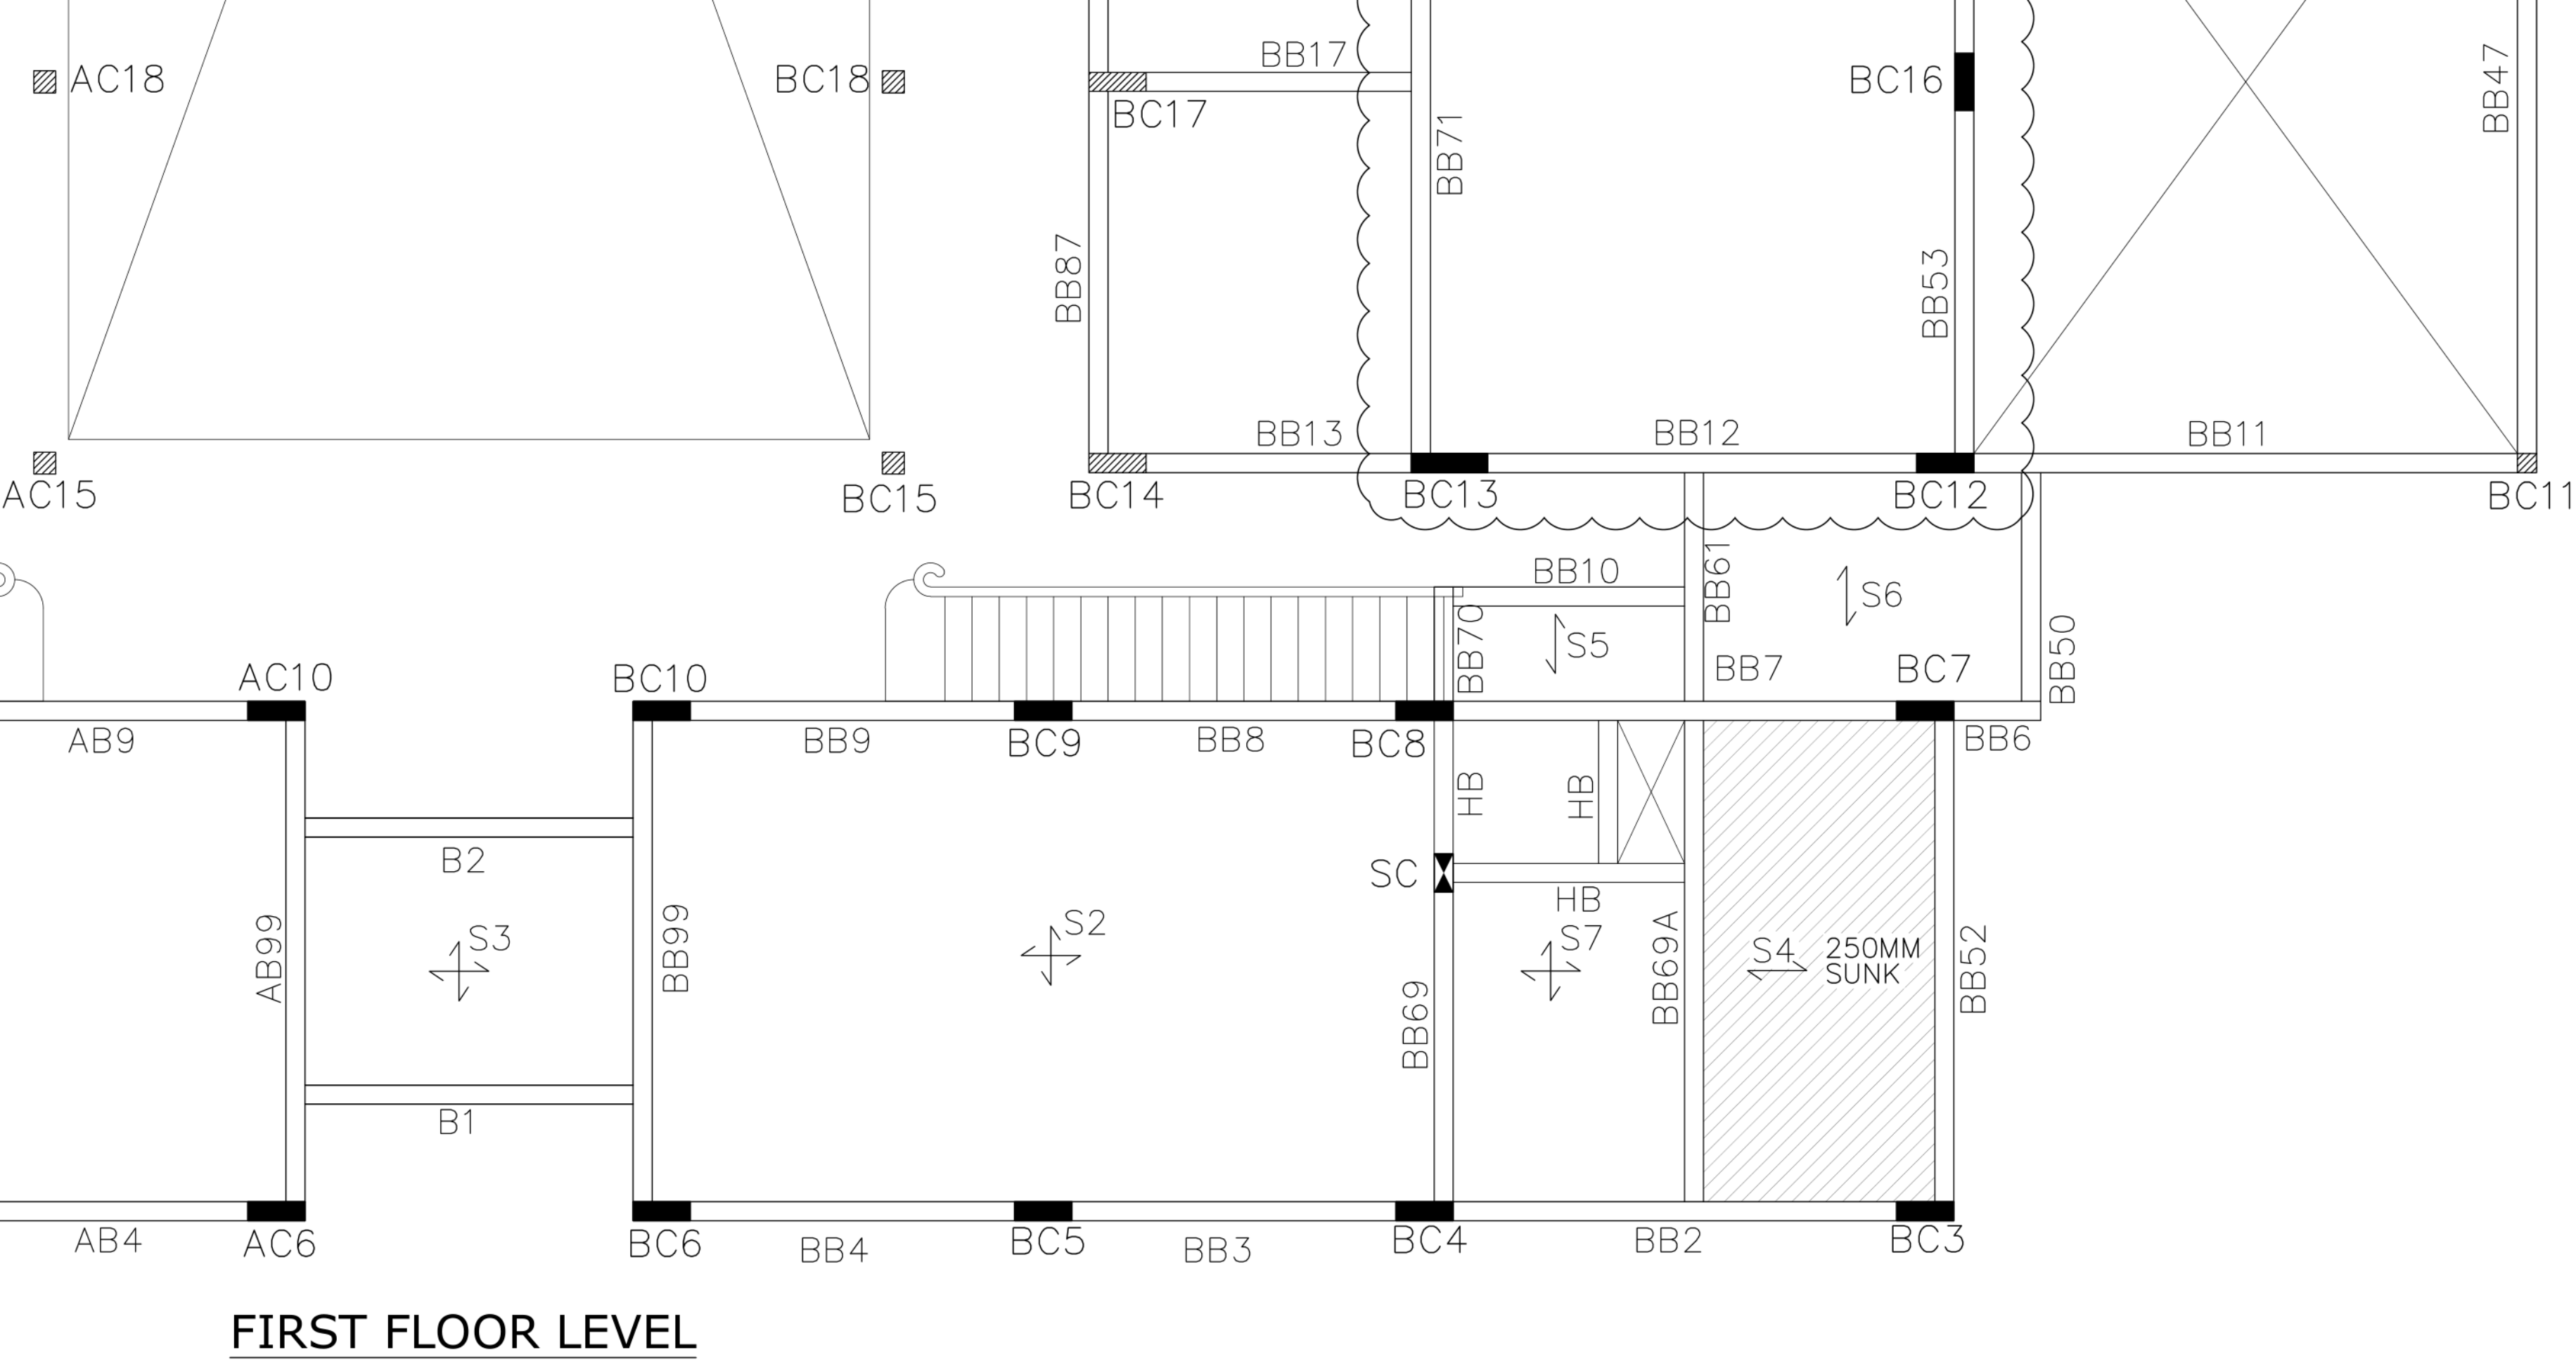

DETAIL OF SC




SIZE :- 200 x 400

STEEL:- 6NOS-T12


LINKS:- T8@150c/c

6NOS-T12

SC COL. FROM GROUND FLOOR LVL.
TO 1ST FLOOR LVL.

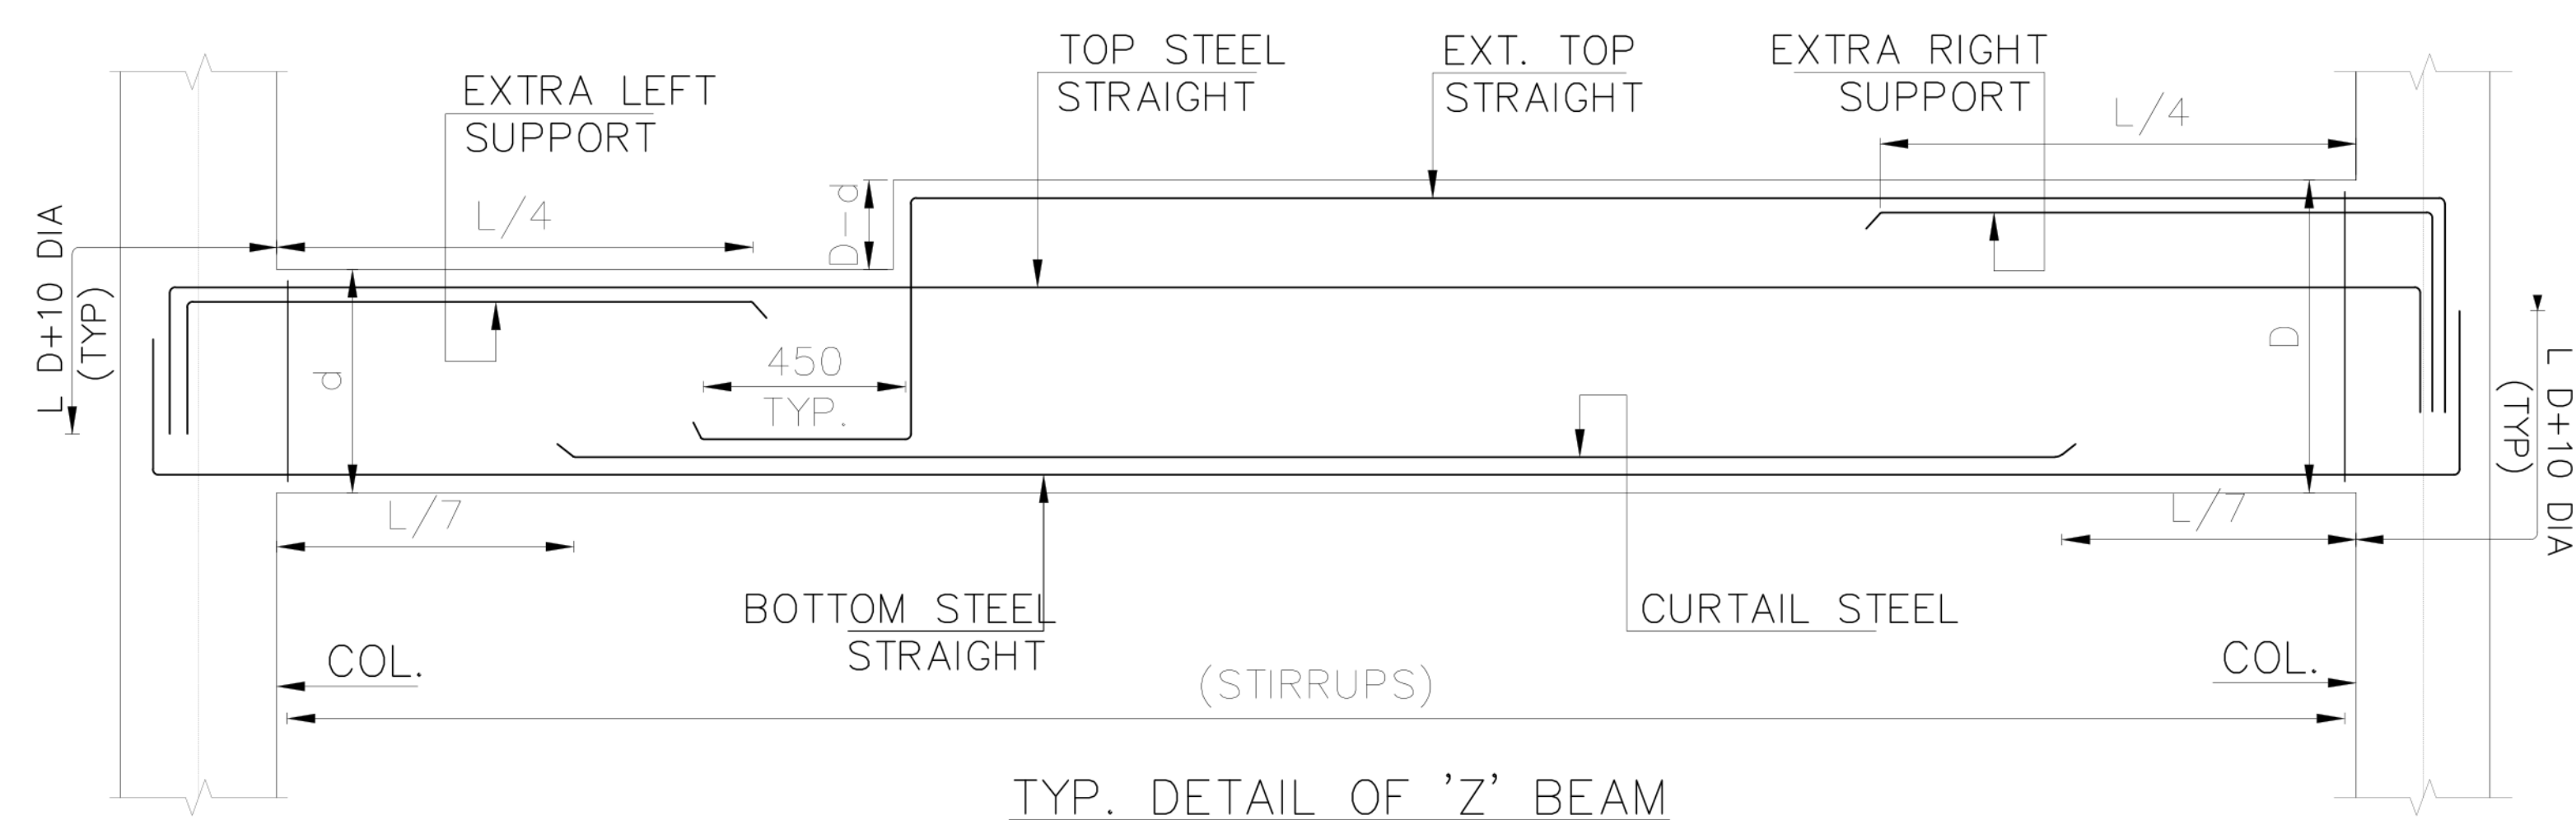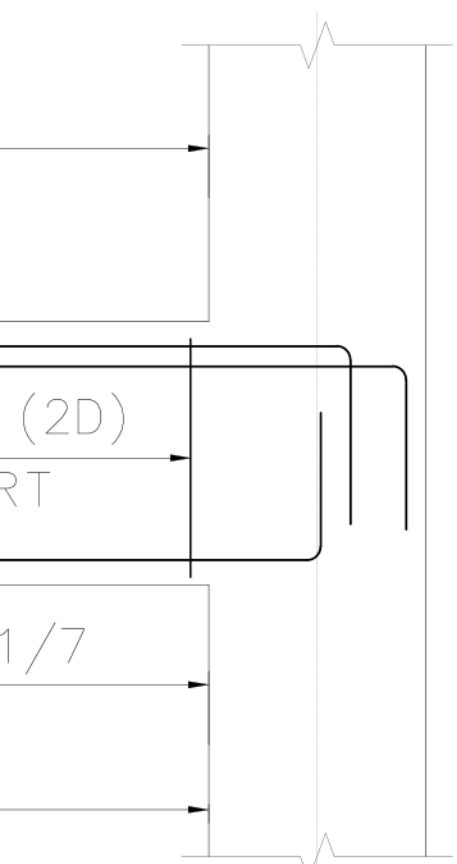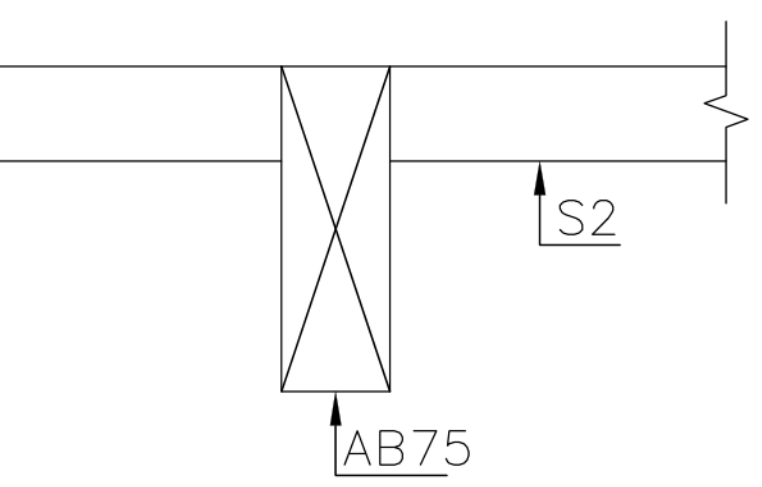

TYP. DETAIL OF 'Z' BEAM

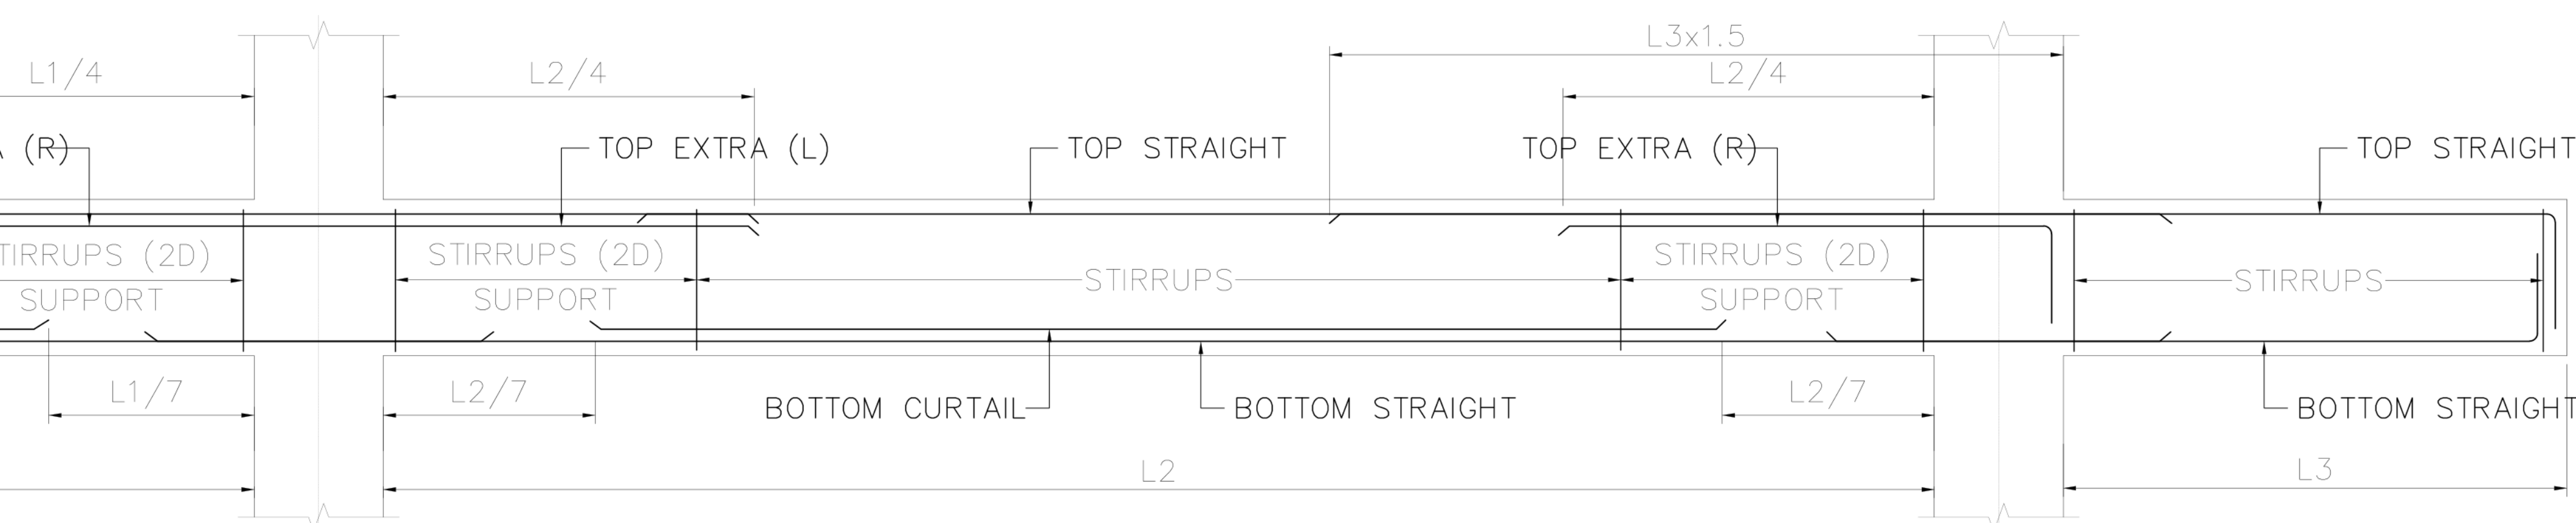

OF SPECIAL CONFINING REINFORCEMENT REQUIREMENT FOR BEAM REINFORCEMENT