

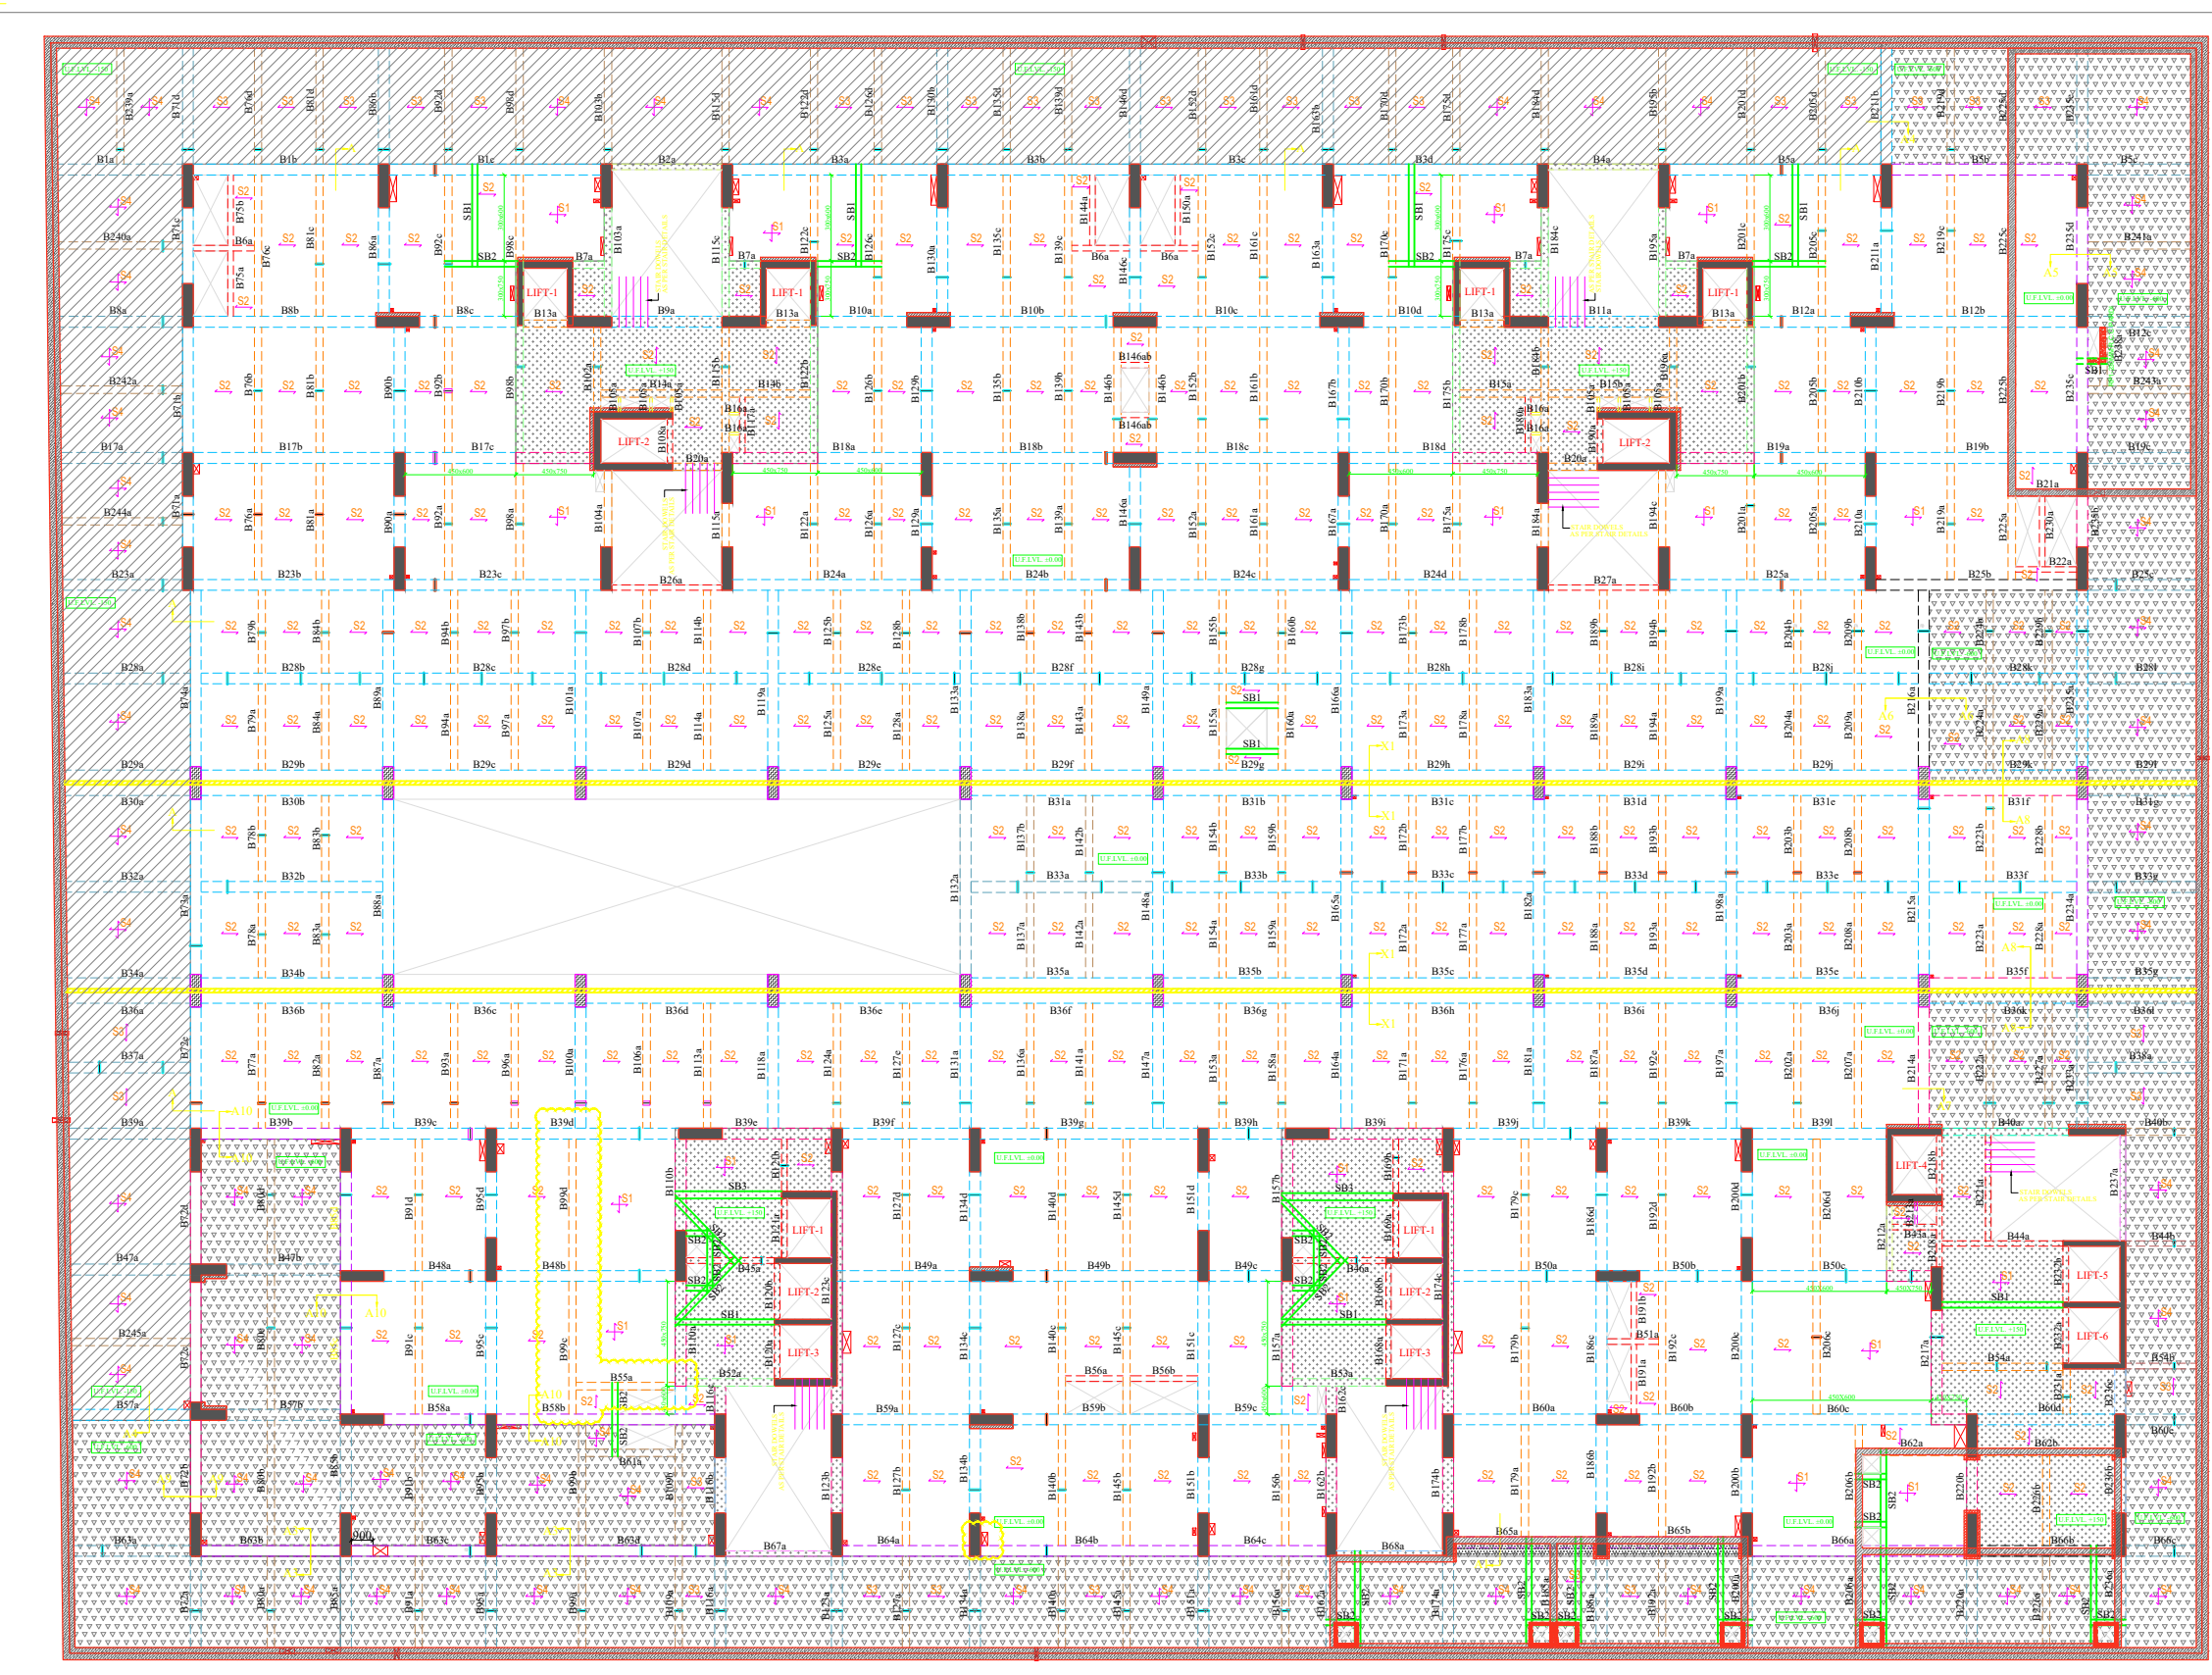












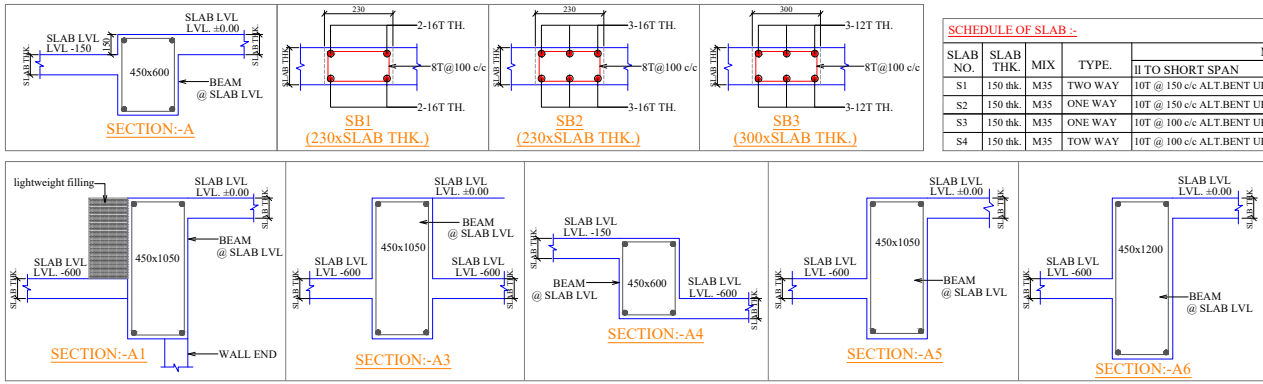


STRUCTURAL LAYOUT @ 1ST BASEMENT ROOF SLAB LVL
*FOR ALL CENTER LINE DIMENSIONS & LOCATION REFER ARCH. DRG.

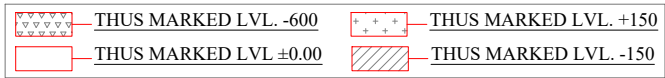

SCHEDULE OF SLAB :-

SLAB NO.	THK.	MIX.	TYPE	MAIN STEEL	EX. TOP OVER SUPPORT	DIST. STEEL
S1	150mm	M35	TWO WAY	IT TO SHORT SPAN	IT TO LONG SPAN	IT TO LONG SPAN
S2	150mm	M35	ONE WAY	IT TO SHORT SPAN	IT TO LONG SPAN	IT TO LONG SPAN
S3	150mm	M35	ONE WAY	IT TO SHORT SPAN	IT TO LONG SPAN	IT TO LONG SPAN
S4	150mm	M35	TWO WAY	IT TO SHORT SPAN	IT TO LONG SPAN	IT TO LONG SPAN

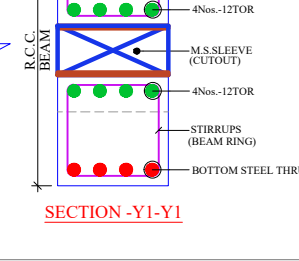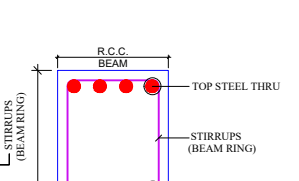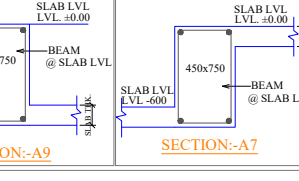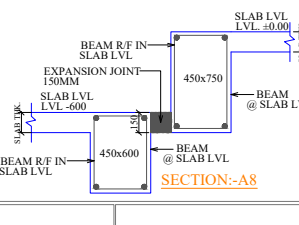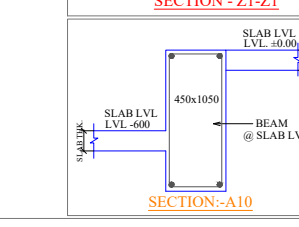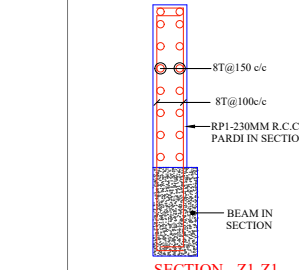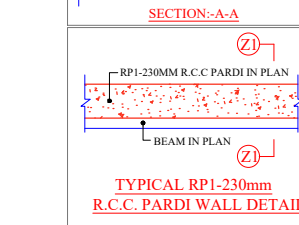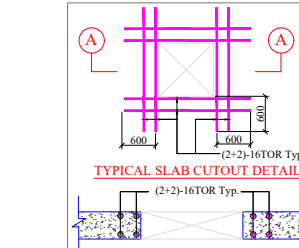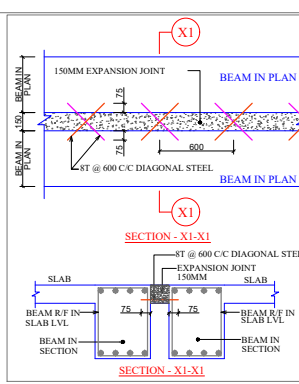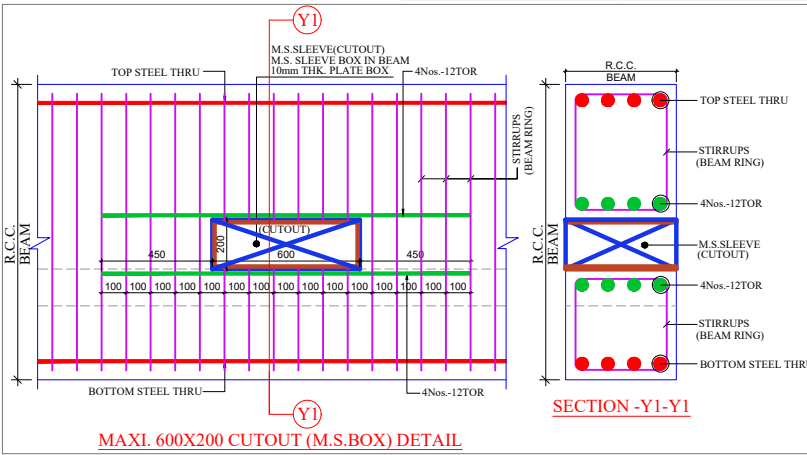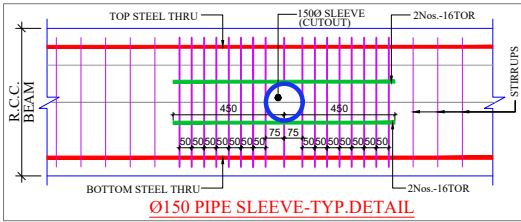

GENERAL NOTES :-
* ALL CONCRETE MIX M-35 OR OTHERWISE SPECIFIED. MACHINE MIXED & VIBRATED.
* EXECUTION OF WORK SHOULD BE CARRIED OUT AS PER NBC & INDIAN STANDARD.
* ALL CONSTRUCTION MATERIAL SHOULD BE CONFIRM TO RELEVANT INDIAN STANDARD.
* SOIL REPORT DOSE NOT INDICATE ANY CHANCES OF LIQUIFICATION.
* THIS DRAWING IS BASED ON ARCHITECTURAL DRAWING.
* CUBE TEST FOR EACH CASTING SHOULD BE CARRIED OUT & SUBMITTED TO US.
* TESTING OF CEMENT (OTHER THAN FACTORY TEST RESULT) SHOULD BE CARRIED OUT FOR ANY CEMENT BRAND LIKE J.K., J.K. LAXMI, BINANI, J.K.VIJAY STAMBH OR ITS EQUIVALENT.

STR. CONSULTANT : ARCHITECTS : ARCH. CONSULTANT :
EXECUTION
HM ARCHITECTS
MEP CONSULTANT


NOTE:-
* ALL SUNK TO BE FILLED WITH LIGHT WEIGHT MATERIAL HAVING MAXIMUM DENSITY OF 600 kg/cu.m

REVISIONS :-

NO.	REMARKS
R1	1ST BASEMENT ROOF SLAB LVL REVISED AS PER ARCH.DETAIL DWG.

PRINTS ISSUED :-

NOS.	E-mail App	E-mail App	E-mail App	E-mail App	E-mail App	E-mail App
DATE	28/01/21	24/03/21	09/06/21	22/06/21	28/06/21	06/09/21
NOS.	E-mail App	E-mail App	E-mail App	E-mail App	E-mail App	E-mail App
DATE	29/09/21	08/10/21	27/10/21	29/10/21	30/10/21	20/11/21
NOS.	E-mail App	E-mail App	E-mail App	E-mail App	E-mail App	E-mail App
DATE	22/11/21	23/11/21	02/12/21	16/12/21	17/12/21	
APPROVAL						
TENDER						
ADVANCE GFC						
GOOD FOR CONSTRUCTION						

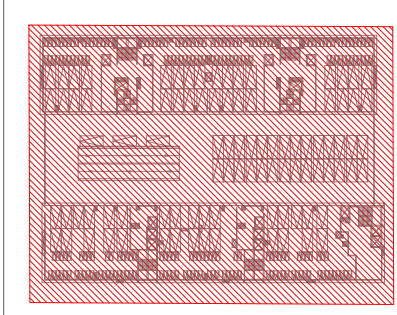

ARCHITECTS :
HM ARCHITECTS
HM ARCHITECTS
e:contact@hmarchitects.in

STRUCTURE CONSULTANT :
SETU INFRASTRUCTURE
D 701-704 The first, 8th, Keshav Baug Party Plot Judges Bungalow Road,
Off 132/3 Ring Road, Vadgaon, Ahmedabad - 380015
Phone : 079 - 40037661, 26751800
E-mail : setuinf@gmail.com

PROJECT NAME :
2055 VENUS PASHMINA
- AHMEDABAD
DRG. NO. : VP / CLUSTER-A-B / BLOCK ABCDE / 04
TITLE : 1st BASEMENT ROOF SLAB LVL PLAN AND DETAIL
SCALE : N.T.S. PRINT SIZE : A1
DRAWN BY : SBP SHEET : 01
CHECKED BY : ZAHIR, N.V.P
DESIGN ENGR. : T.R.S
DATE : 18/06/21
REVISION DATE : 17/12/21

R0